

Joe Anthony Sanchez

Joe.arch.sanchez@gmail.com | (956)579-1369

EDUCATION

Texas Tech University | Lubbock, Tx

B.S.A - Bachelor of Science, Architectural Science

Coursework: Architectural Representation, Architectural Design Studio, Design, Environment & Society, History of World Architecture, Architectural Technology, Fundamentals in Architectural Thinking, Architectural Contemporary Issues, Environmental Analyst-Site Plan

Texas Southmost College | Brownsville, Tx

A.S - Associate of Science, Architectural Science

Coursework: Introduction to Architecture, Architectural Graphics, Architectural Computer Graphics (AutoCAD & Rhino), Architectural Technology, Architectural Design

SKILLS AND TECHNICAL TOOLS

Languages: English (C2), Spanish (C1)

Programs: AutoCad (5 years), Rhino (3 years), Revit (2 years), Sketchup (5 years), Adobe Suite (8 years), Lumion (5 years)

EXPERIENCE

Island Cinema | South Padre Island, Tx

2018-2019

- Managed money and a small team to run the business smoothly
- learned the skills it takes to run a small business and how to handle a team while also having my own responsibilities.

HEB | Port Isabel, Harlingen, and Brownsville, Tx

2019-2022

- Covid respondent to stores in the lower Rio Grande Valley Area.
- Title of “Cross Functional” which included helping produce with orders and stocking, front end with customer service and cashiering; during any shift I would help three to four different departments.

PROJECTS

Friendship of Women “Project Hope” | AutoCAD | Sketchup | Adobe Illustrator

- Provide existing dimensions of interior and exterior of structure
- Provide floor plan for renovation of existing structure
- Confirm proposed floor plan meets owner needs and building code requirements
- Obtain construction permits


City of Brownsville 14th Street Renovation | Rhino | Adobe Illustrator

- Working to help maintain the standard upkeep, maintenance, stewardship of site facilities
- People on the US side wanting to go to Mexico can simply park their car on the US side, walk over to Mexico and have access to several tourist attractions in Matamoros, Mexico.

TABLE OF CONTENTS




RESUME

PLAZA COLORES 14th Street, Brownsville, Tx Sketchup AutoCad Enscape Illustrator	2019
SOL Y LUNA PLAZA Charles and 11th Street, Brownsville, Tx Sketchup Autocad Enscape Illustrator	2020
LUBBOCK COMMUNITY REC CENTER Corner of Glenagoodacre and Ave Q, Lubbock, Tx Rhino Illustrator Model Making (laser cutting, 3d printing, Sketch models)	2021
CHARTER MIDDLE SCHOOL FOR ART AND EDUCATION 26th Street & Upland Avenue, Lubbock, Texas Rhino Revit Adobe	2022

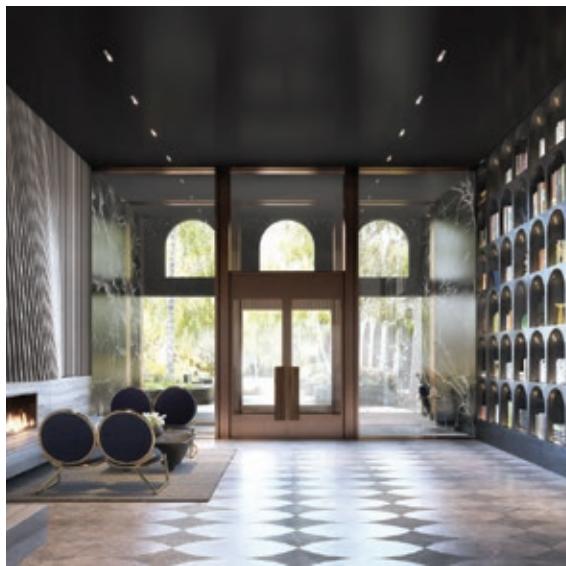


Sol y Luna Plaza




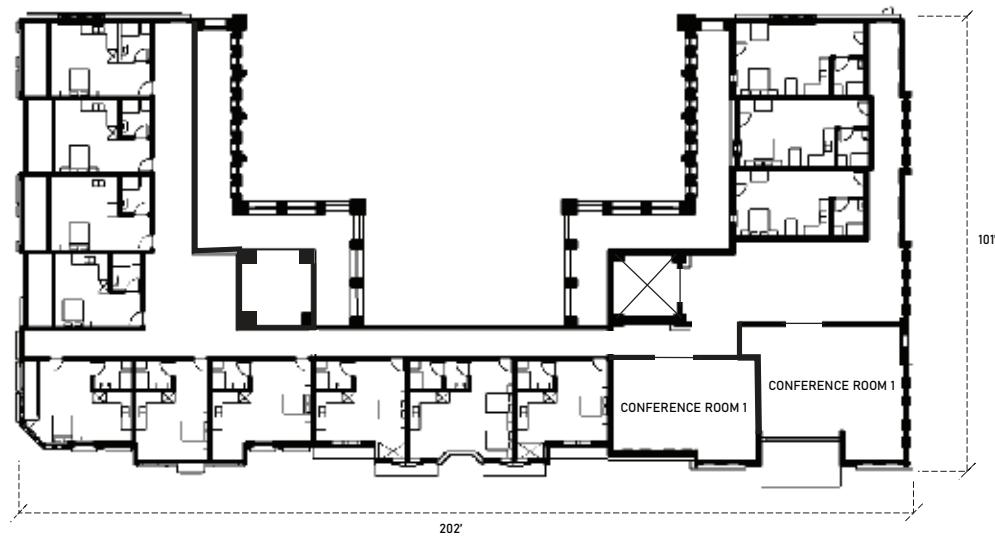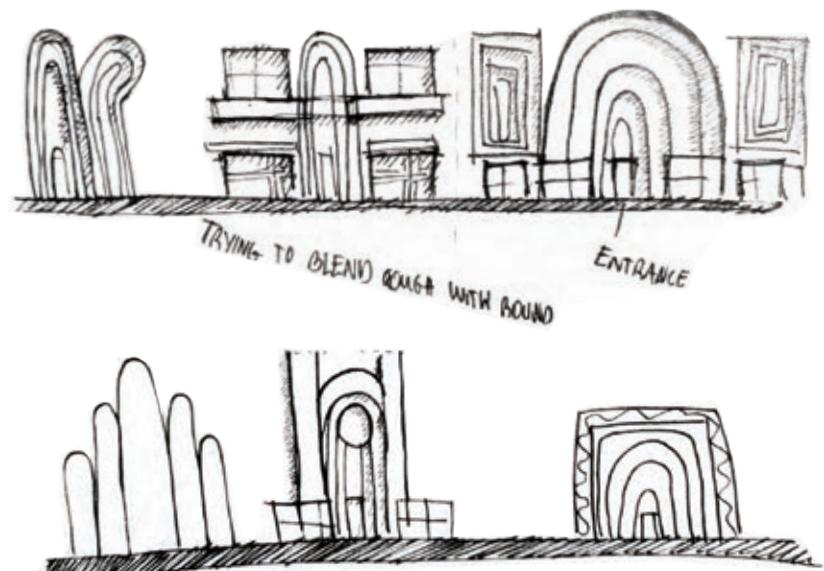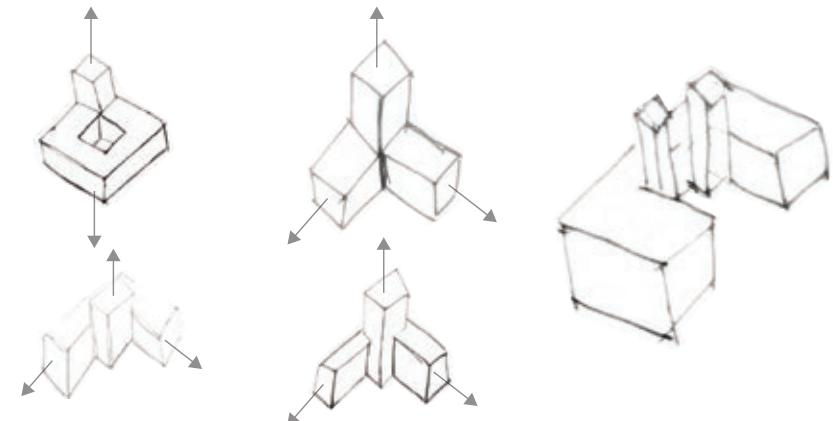













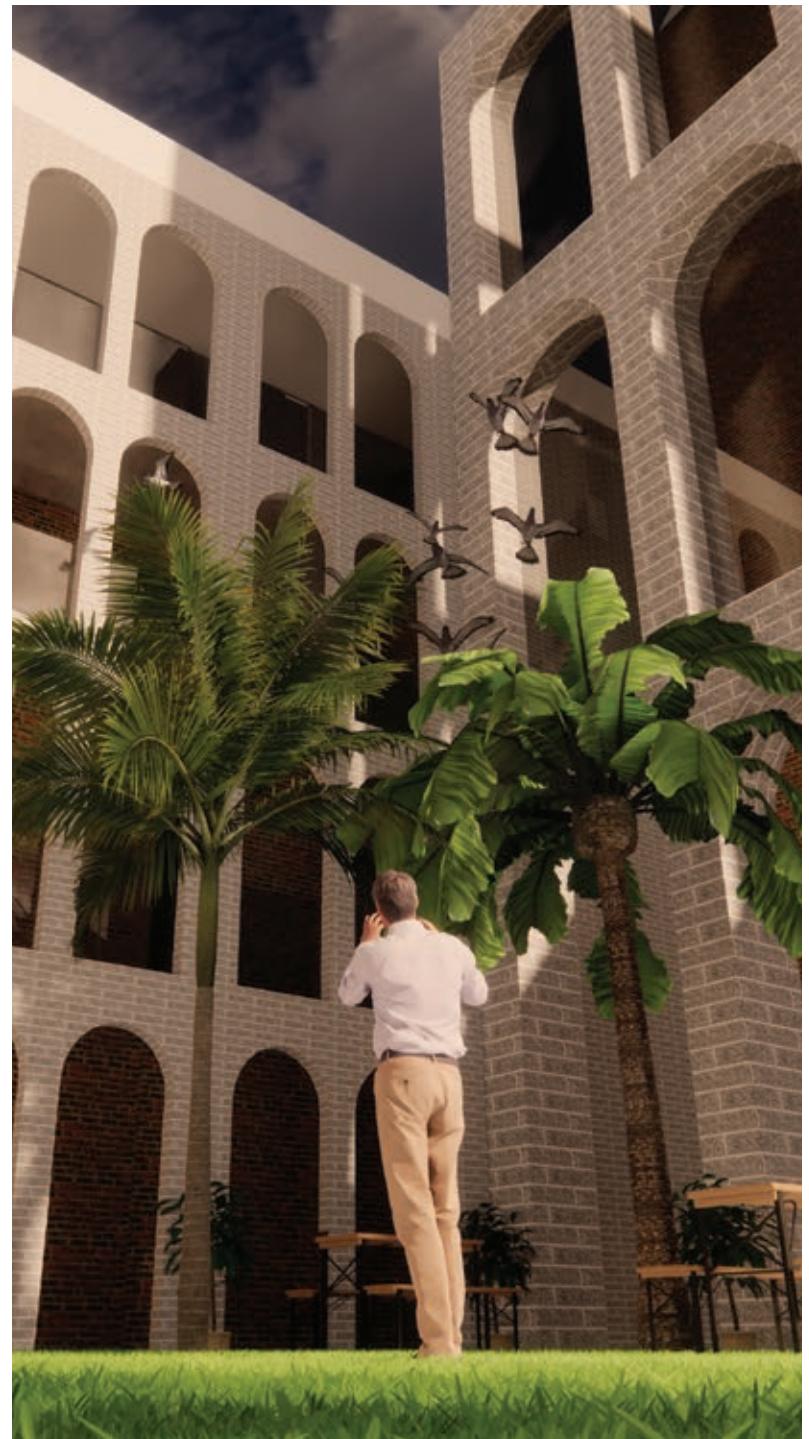

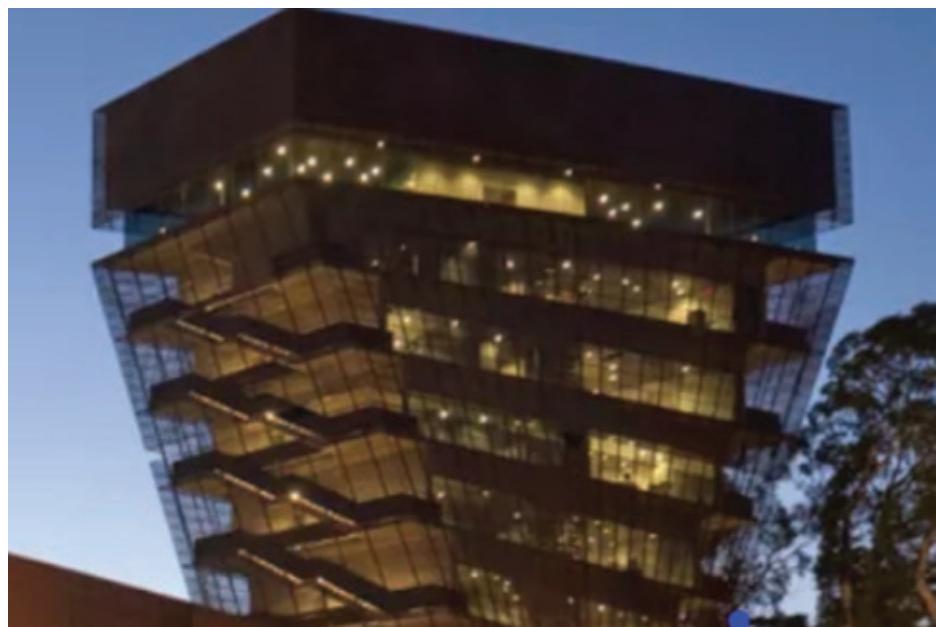


Lubbock Community Rec Center

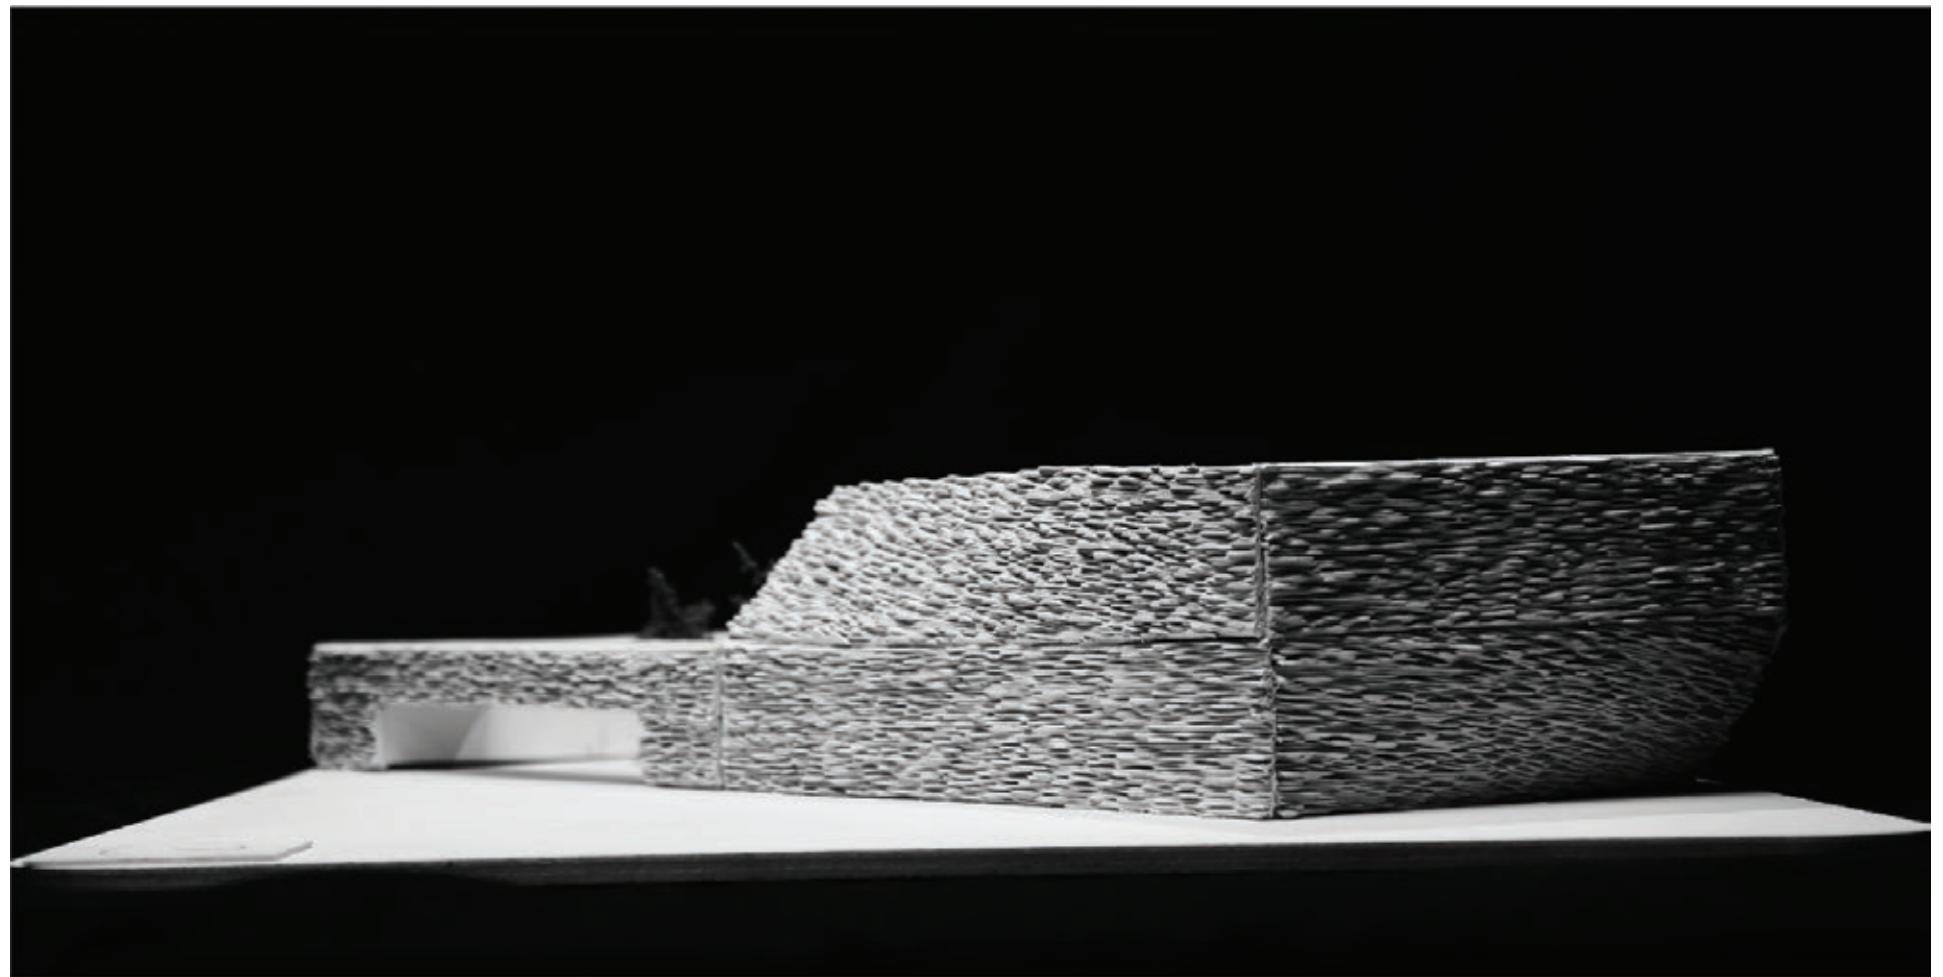


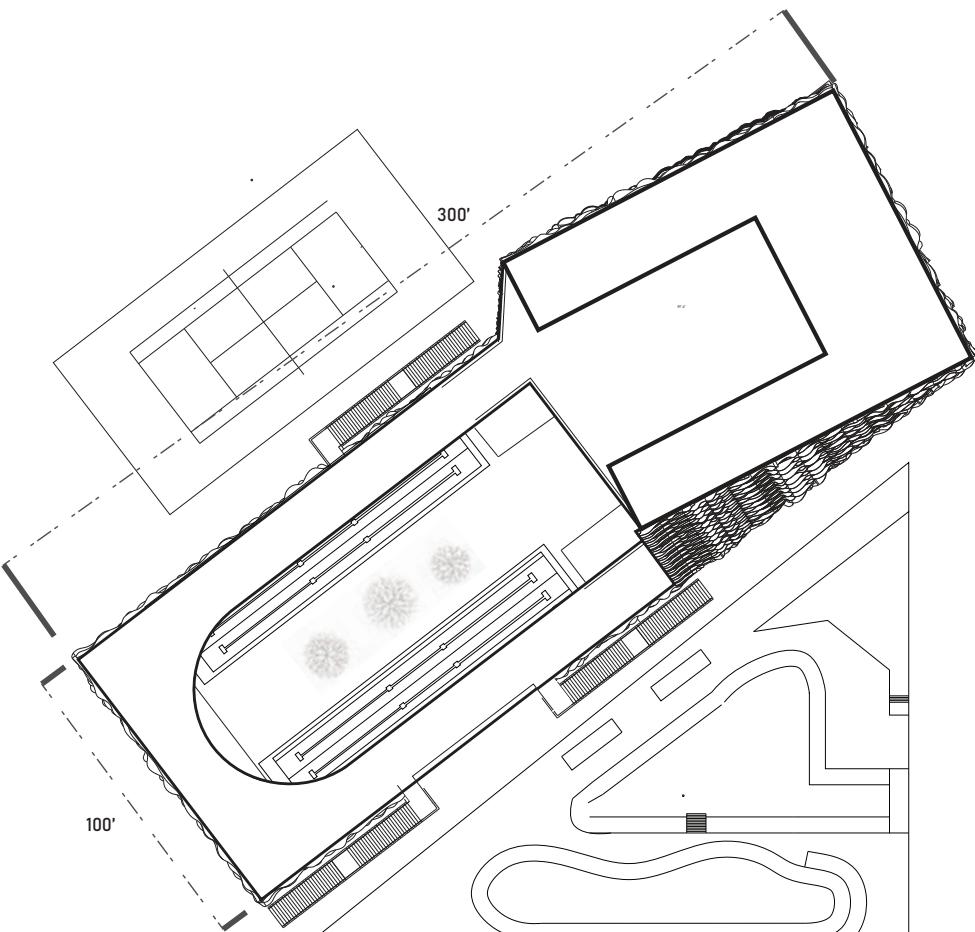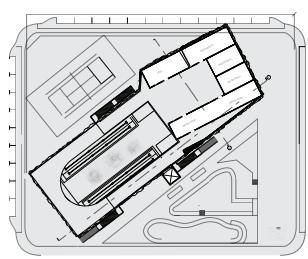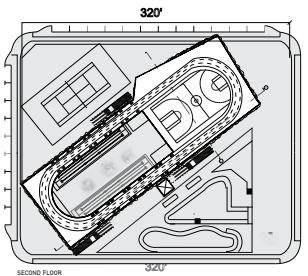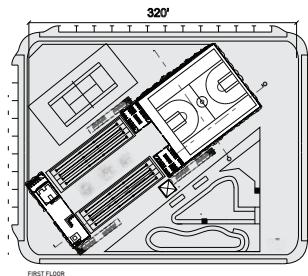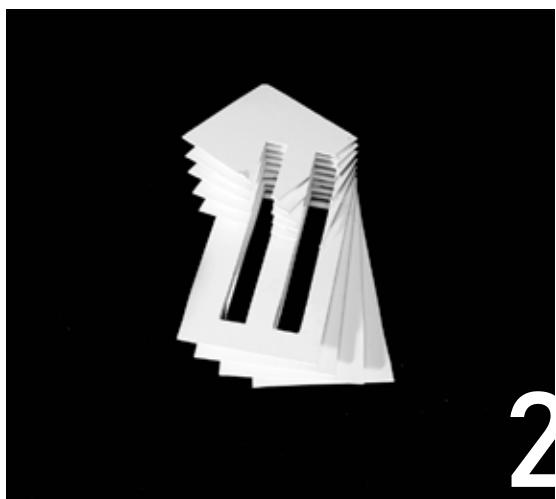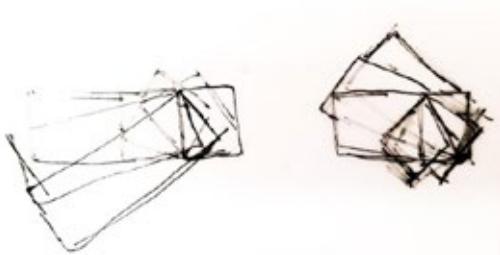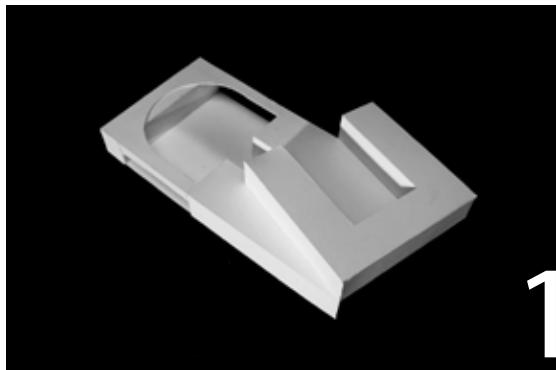


3

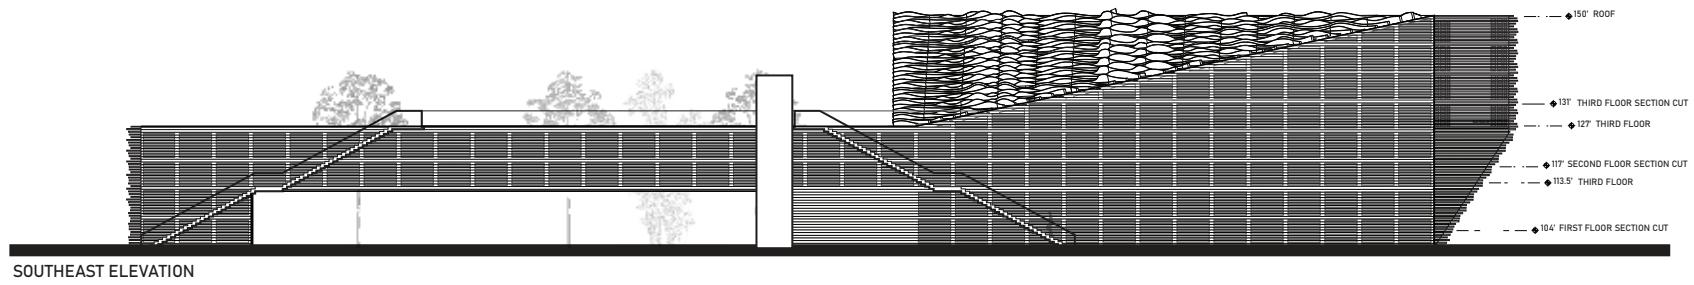


SOUTHEAST ELEVATION

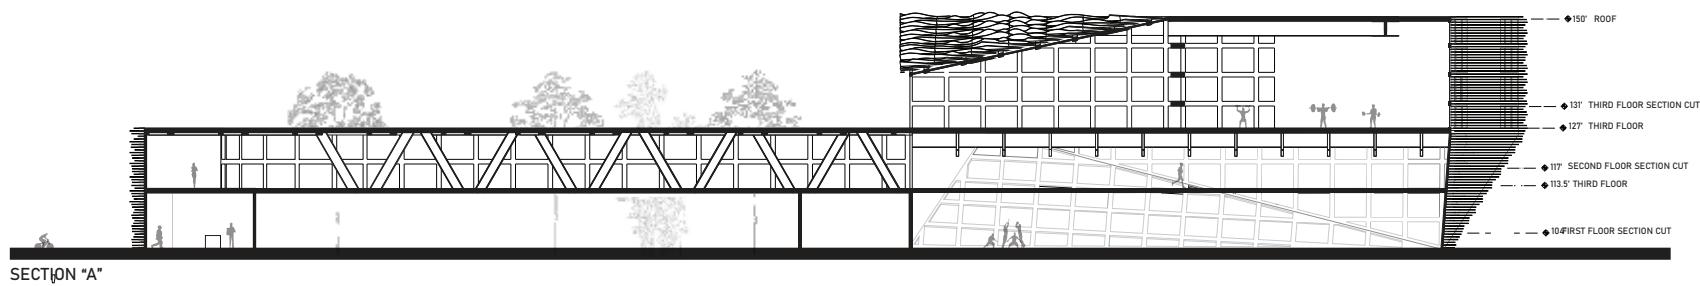


SECTION "A"

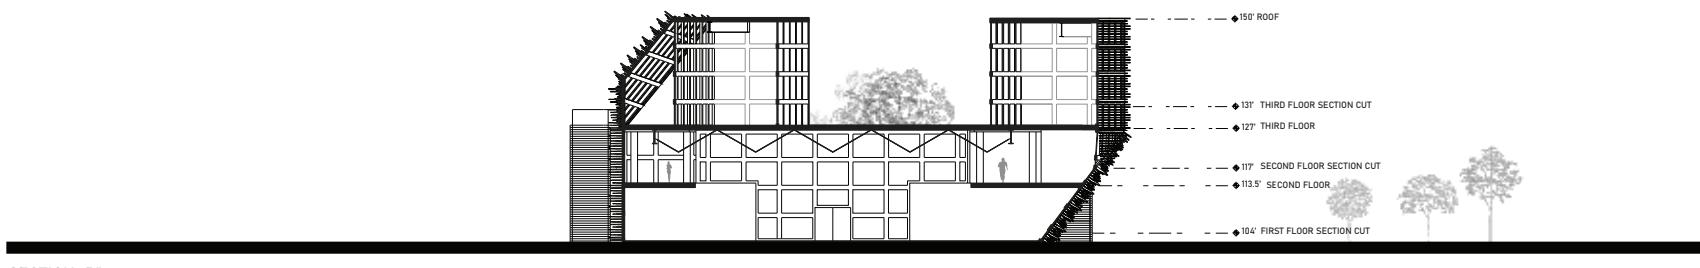


SECTION "B"

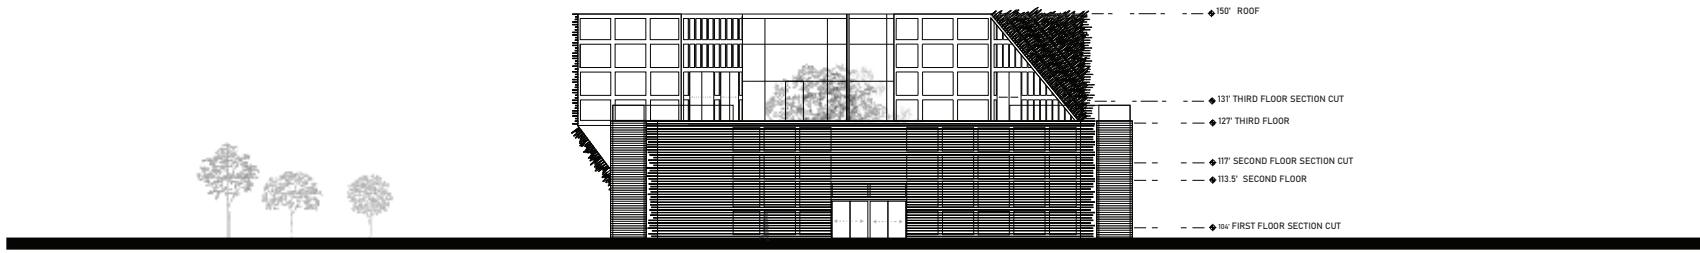

SOUTHWEST ELEVATION

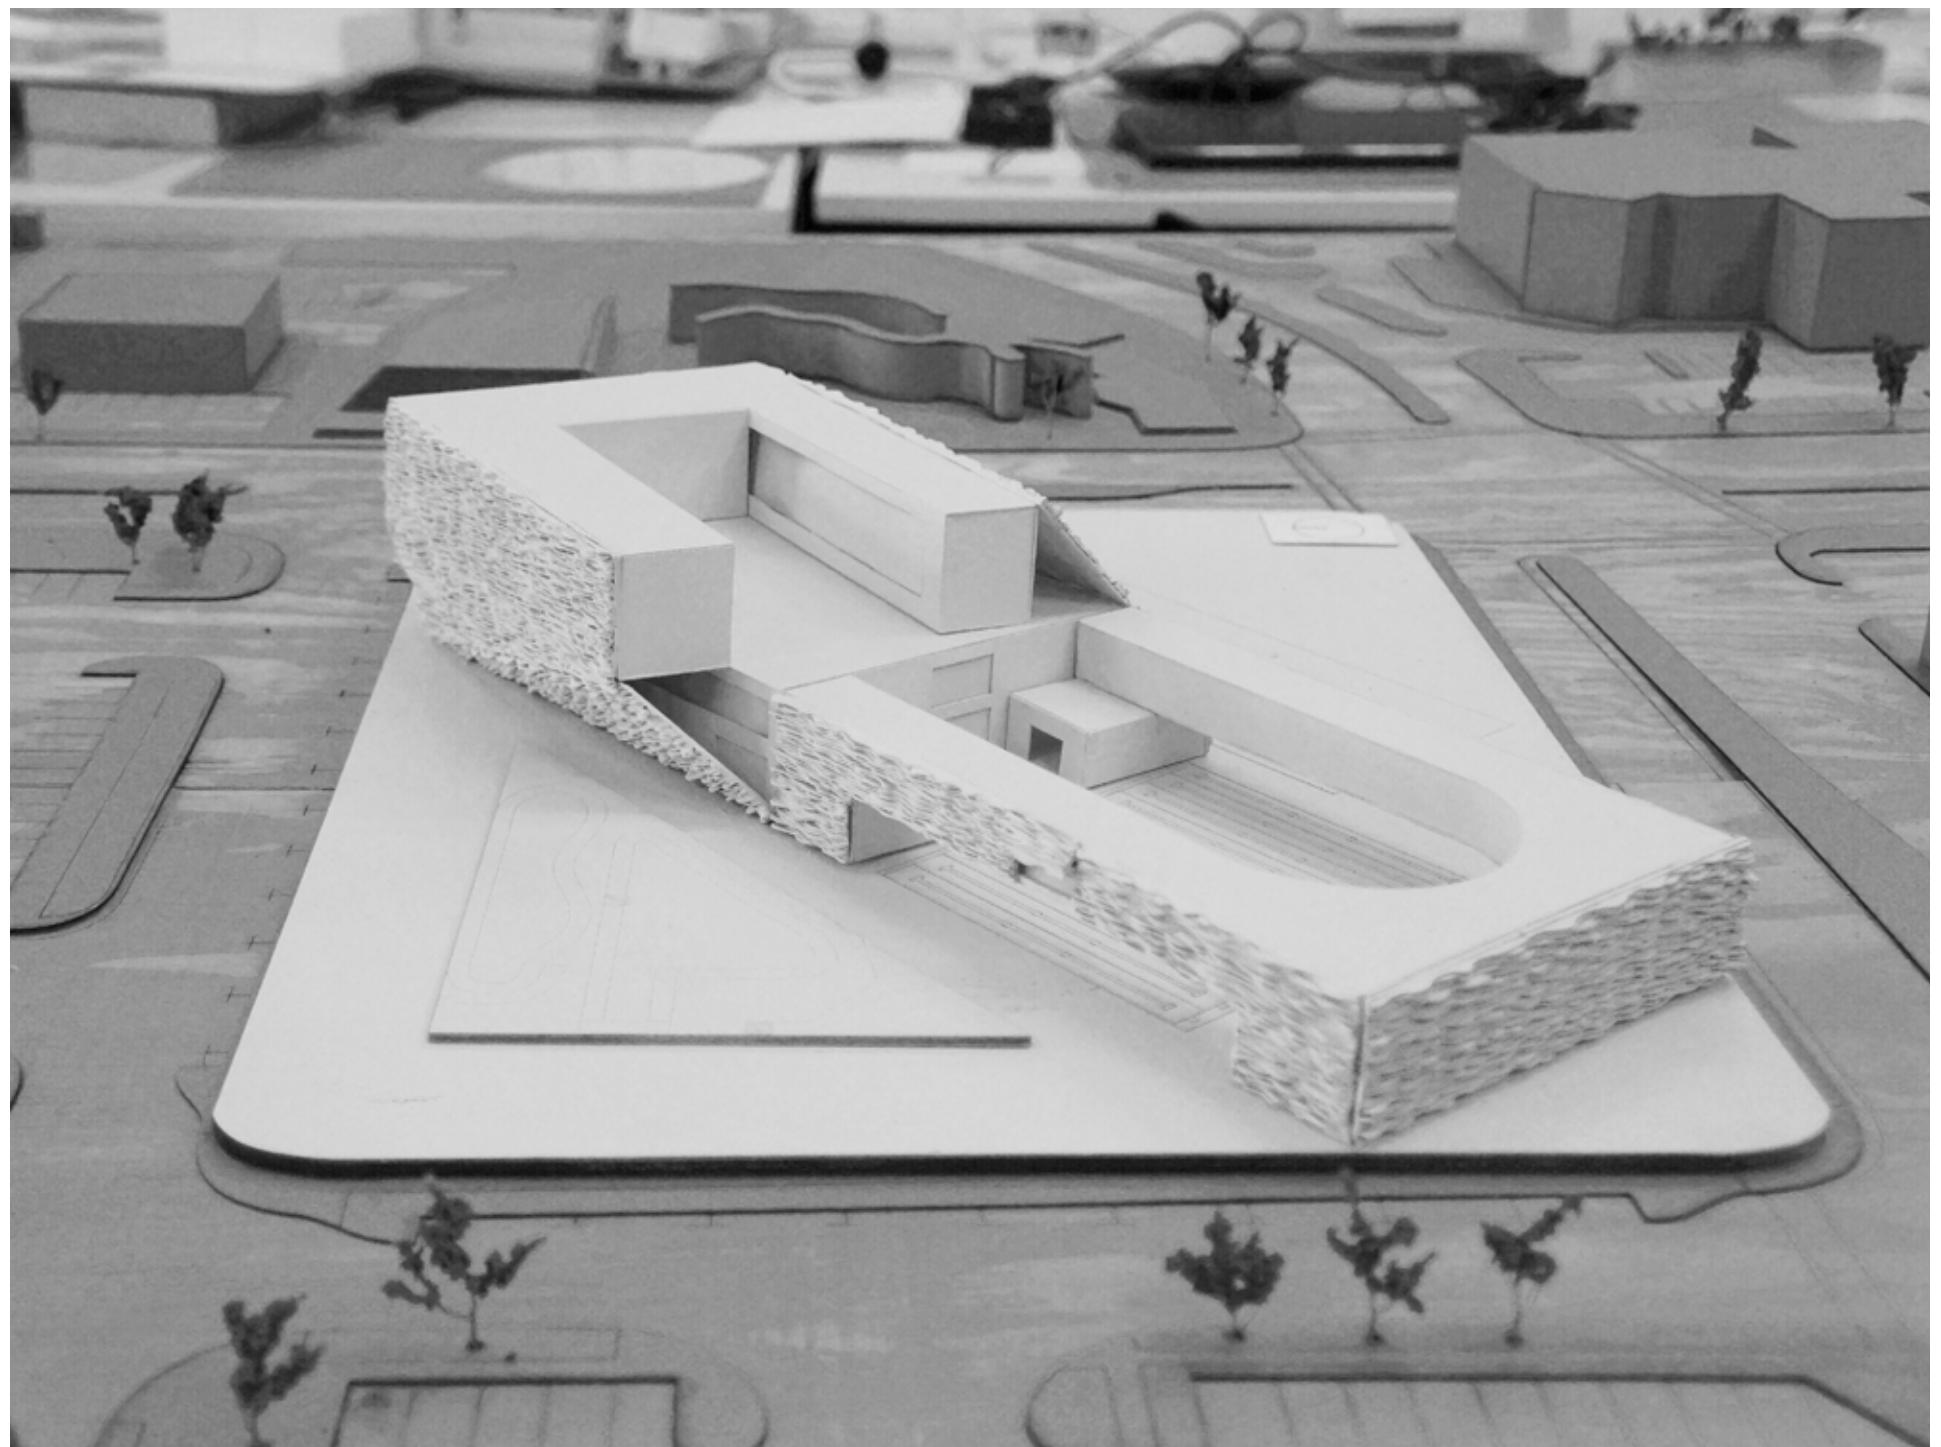

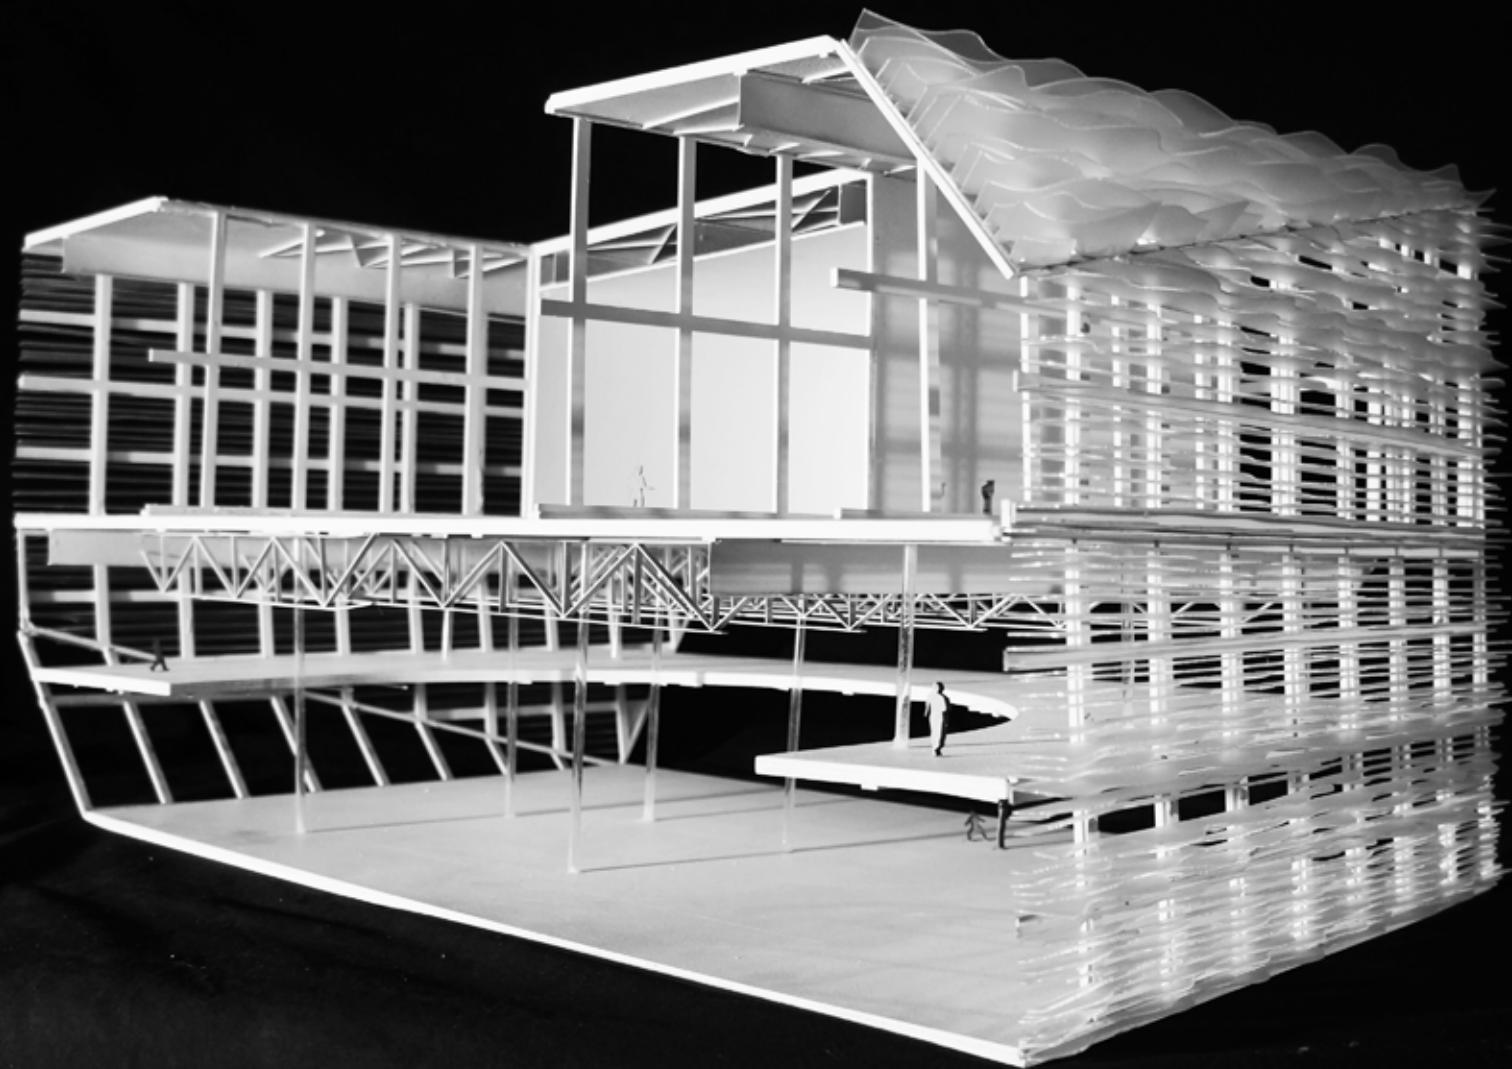







Plaza Colores

14TH STREET

PLAZA COLORES



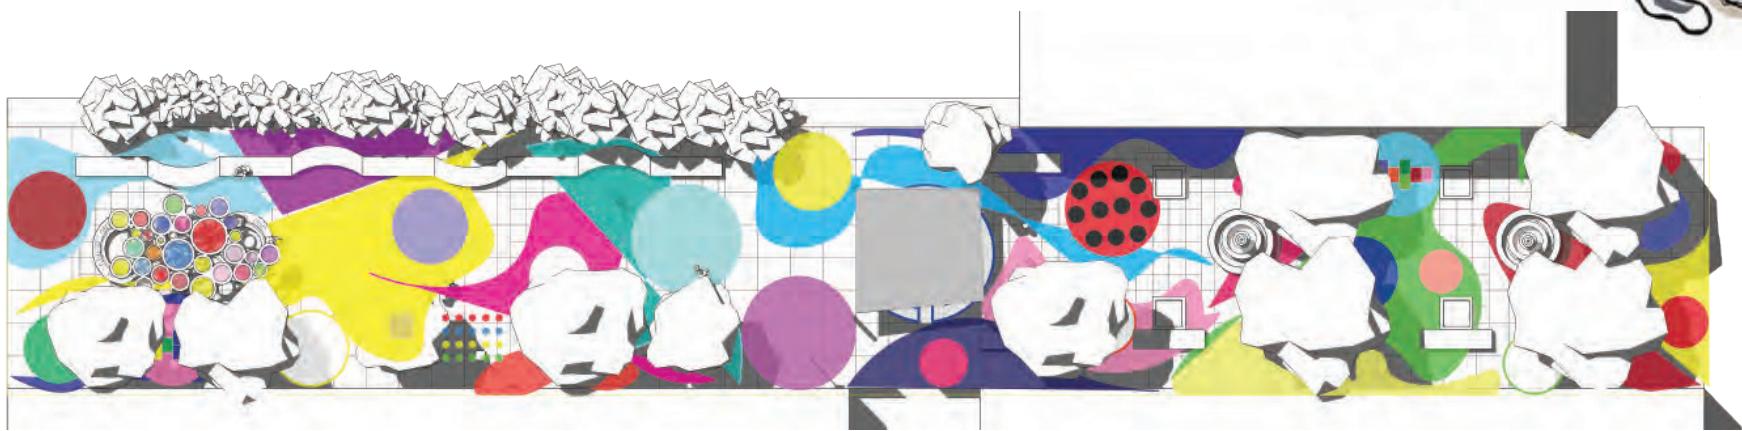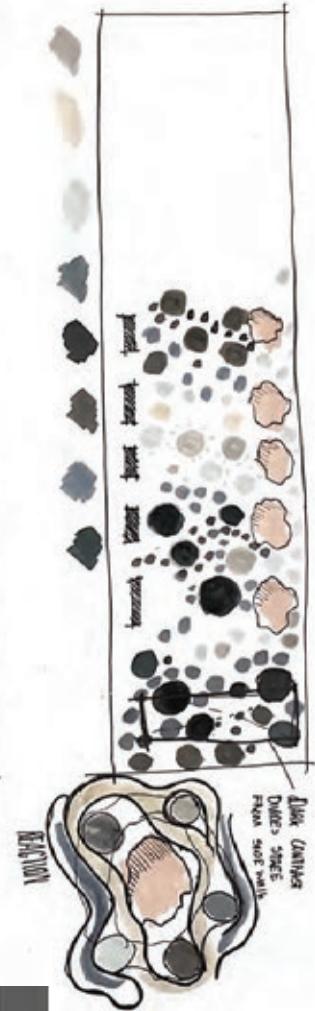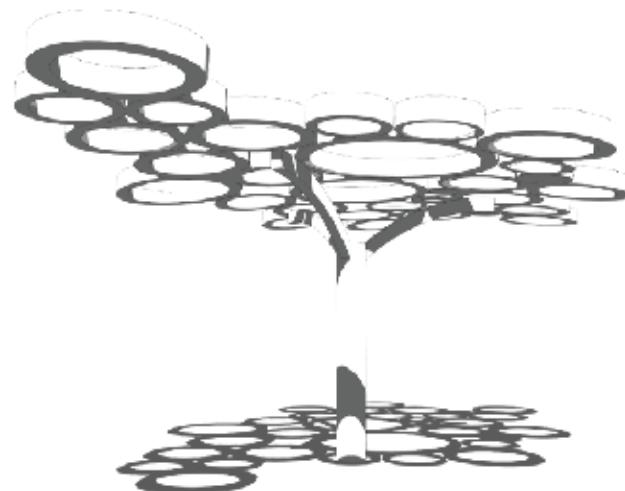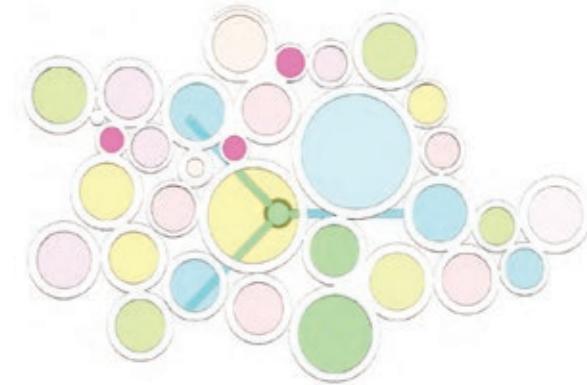










Type	Use	Occupancy
A-2	Classroom	100
A-2	Gym	200
A-2	Library	80
A	Office office	30

CODE ANALYSIS
 OCCUPANCIES
 EDUCATION (E) - PRIMARY OCCUPANCY
 ASSEMBLY (A)
 CAFETERIA (AZ)
 GYMNASIUM, LIBRARY (AJ)
 BUSINESS (B)

AREA CALCULATIONS	
Conference room A	Area 240 sqft
Conference room B	Area 400 sqft
Principals Office	Area 300 sqft
Assistant Principals Office	Area 100 sqft
Teacher Lounge	Area 800 sqft
Office Waiting Area	Area 1000 sqft
Administrators Room	Area 1200 sqft
Administrative Room	Area 375 sqft
Artist Office	Area 300 sqft
Counselor	Area 100 sqft
Diagnostics	Area 100 sqft
Name	Area 250 sqft
Library	Area 3040 sqft
Cafeteria	Area 4000 sqft
Gym	Area 8070 sqft
Art Room 1	Area 1000 sqft
Art room 2	Area 1500 sqft
Classrooms	Area 9000 sqft
Bathrooms	Area 2200 sqft
Total	25,907 sqft





CONSTRUCTION TYPE

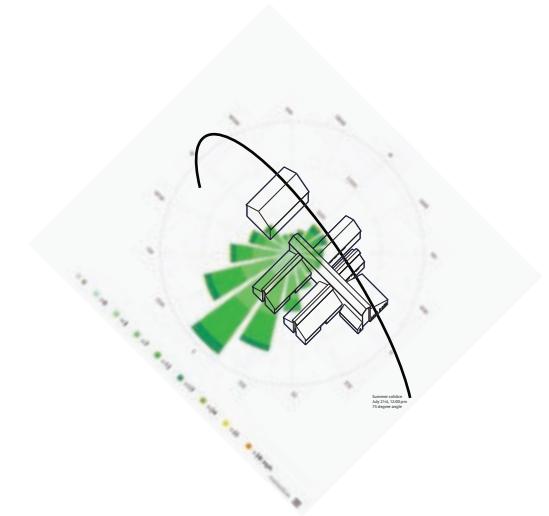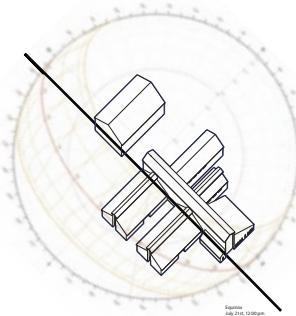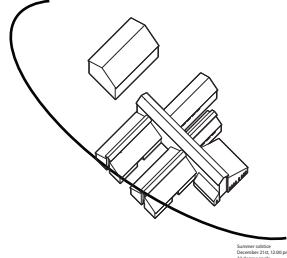


TEA STANDARDS


ACCESSIBILITY



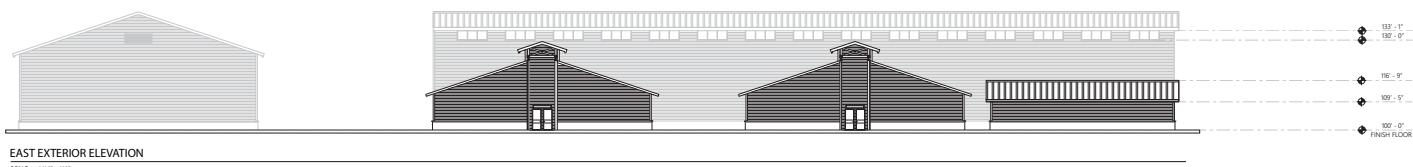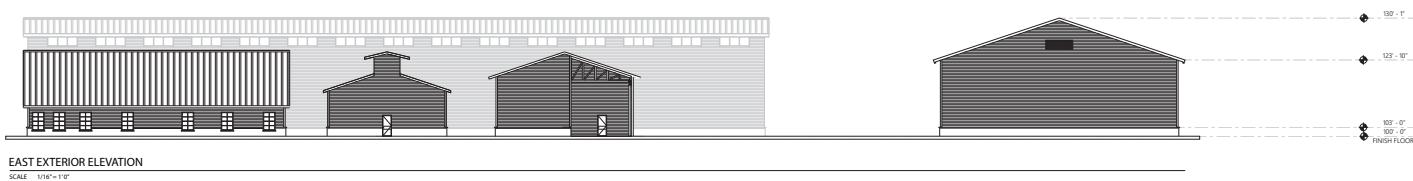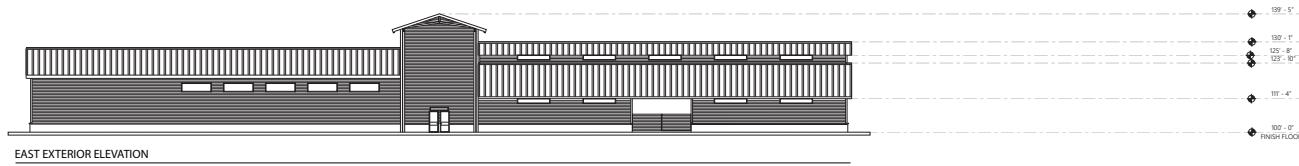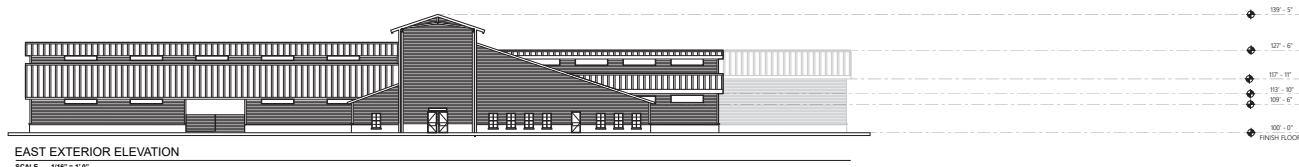


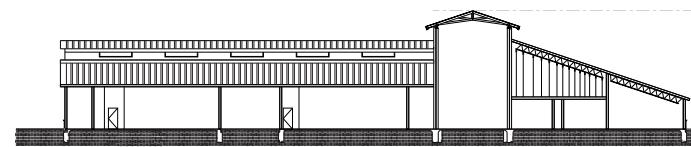


EAST EXTERIOR SECTION
SCALE 1/16" = 1' 0"

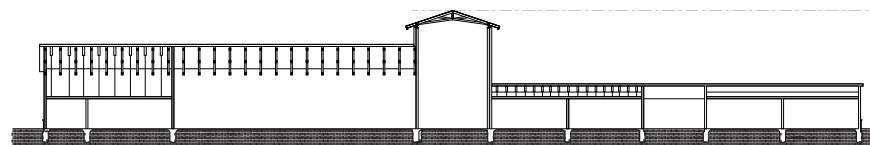

EAST EXTERIOR SECTION
SCALE 1/16" = 1' 0"

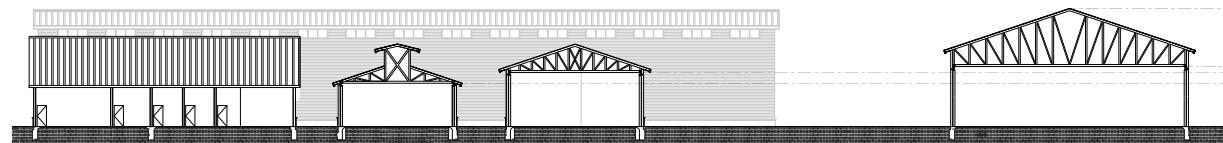

EAST EXTERIOR SECTION
SCALE 1/16" = 1' 0"

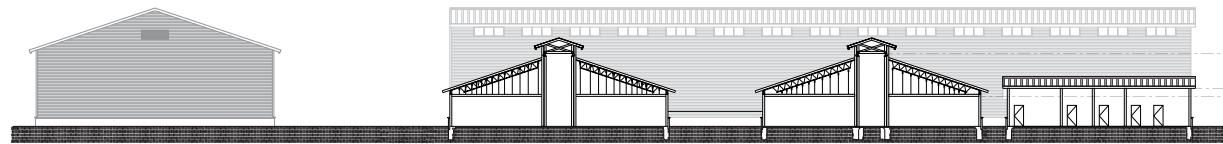

EAST EXTERIOR SECTION
SCALE 1/16" = 1' 0"

